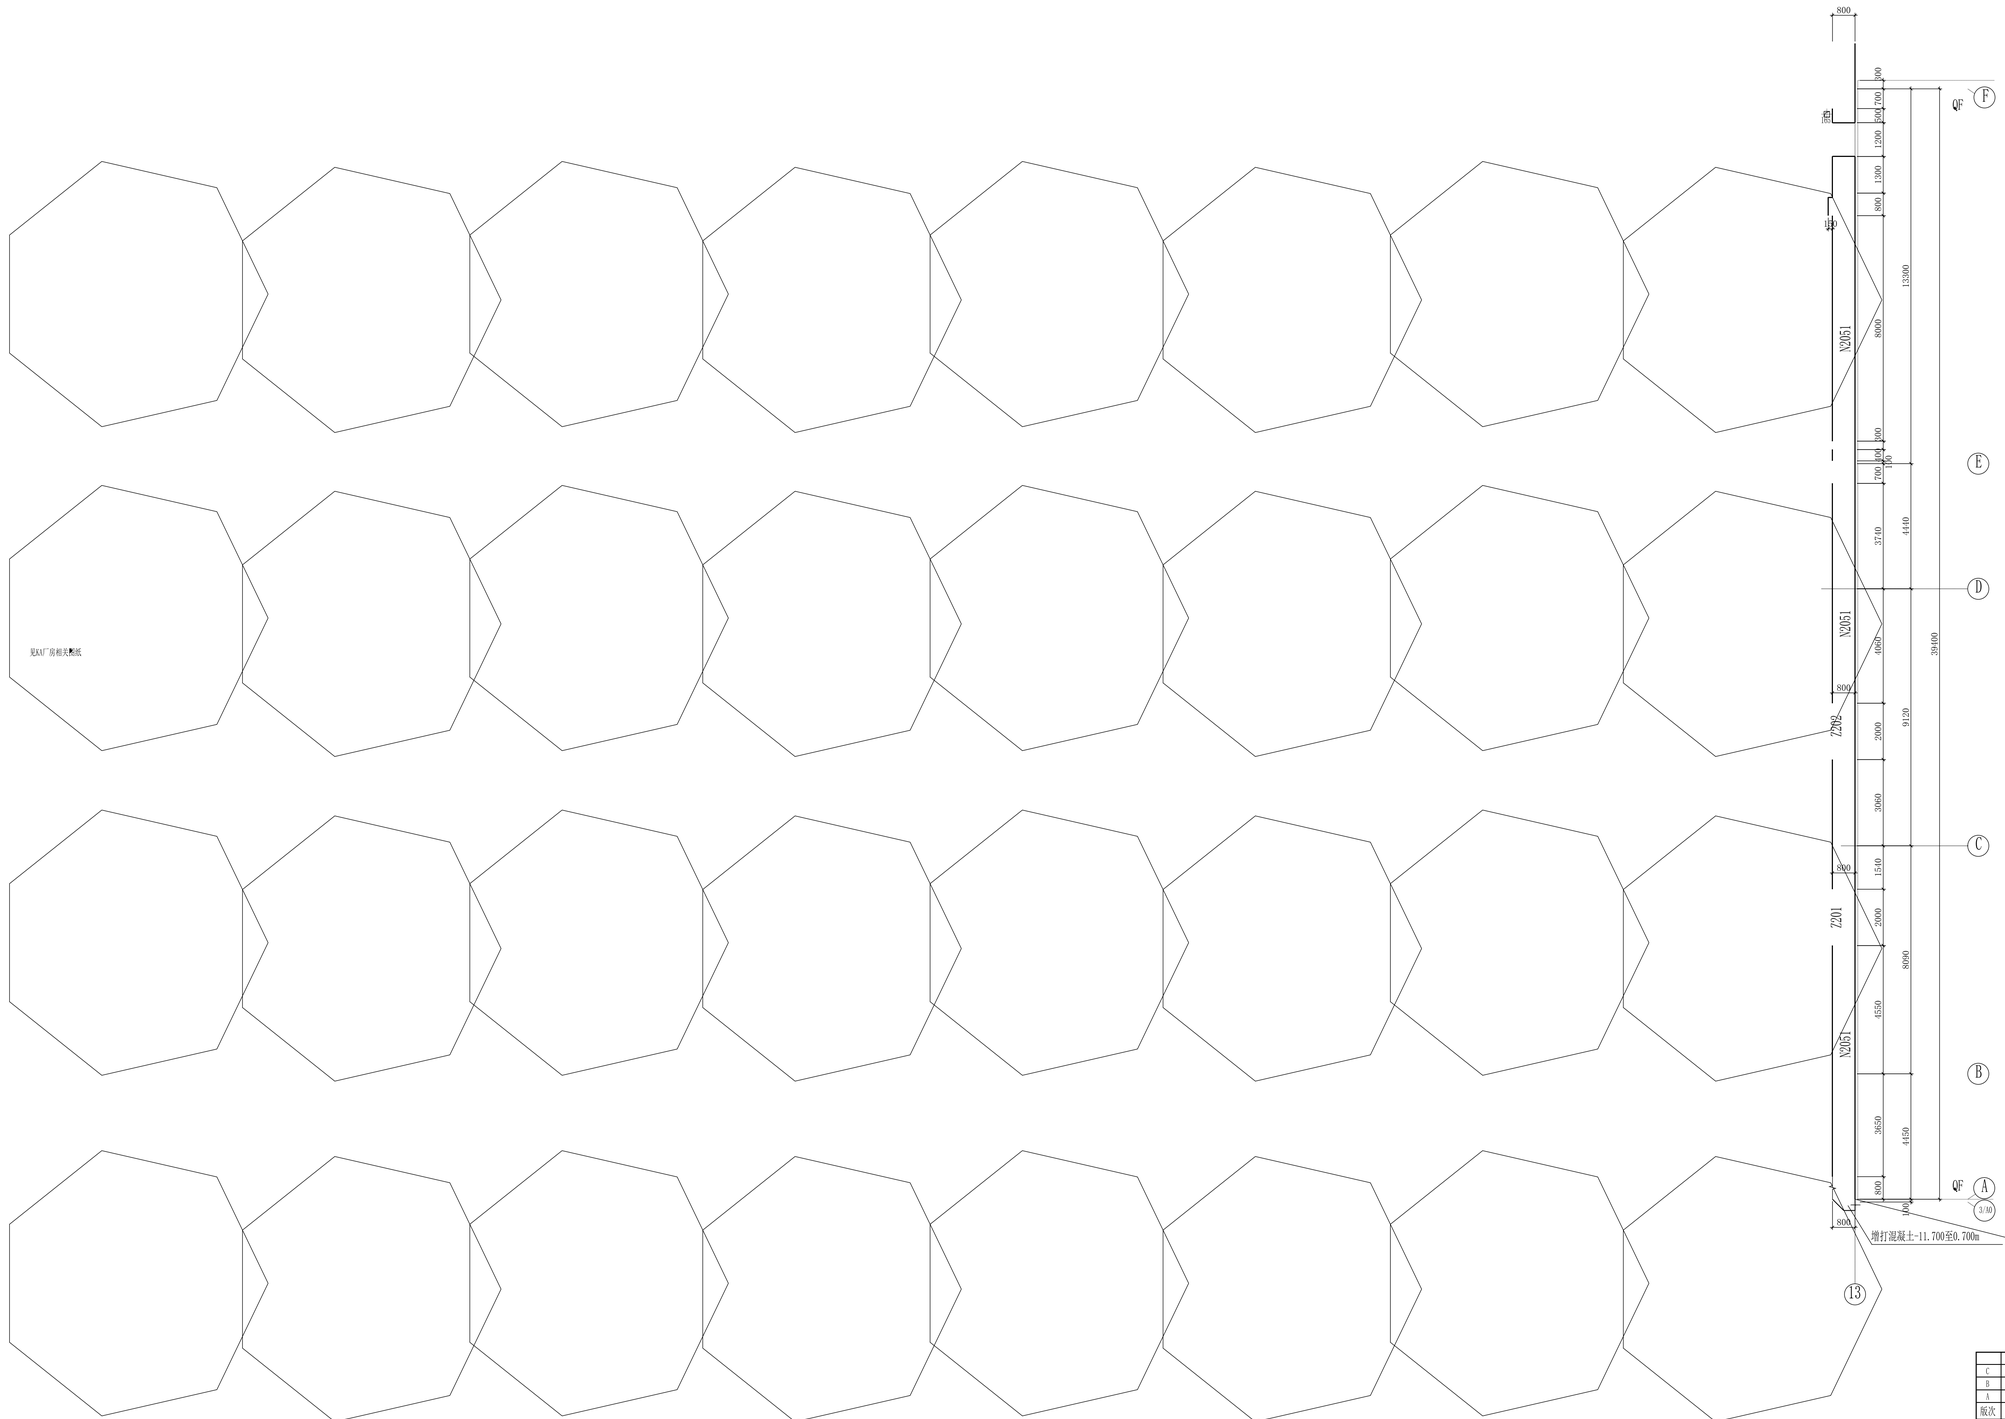

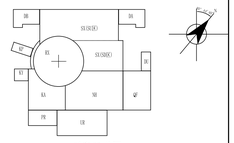

厂房索引图

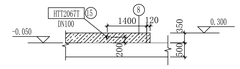

a-a

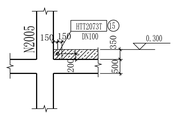

b-b

通用节点代码

		相关技术规格书
1	止水带	CP05JT1014
2	嵌缝	CP05JT1016
3	铁丝网模板	
4	为二次浇灌混凝土凿毛50mm	
5	为二次浇灌混凝土预埋φ250钢板网管	
6	用于二次浇灌的φ100排气孔	
7	二次浇灌混凝土	
8	矮墙或翻边(二次浇灌)	
9	混凝土垫层(找坡混凝土)	CP05JT0119/20
10	可拆式混凝土墙	
11	可拆式砌块墙	
12	门洞企口150x150mm	
13	地漏	2016JT1018
14	纤维水泥套管	CP05JT1011
15	钢套管	CP05JT1011
16	预埋件	CP05JT1011
17	不锈钢覆面	
18	混凝土镶入卡轨	CP05JT0503

相关施工图

模板图:
配筋图:
钢筋表:

附注:

1. 图中未注明处楼板顶标高均为-0.050m,厚500mm.
2. 未注明门洞企口均为 .
3. 统计表中方孔的规格为"XxY",X长度方向与自定义参考坐标X长度方向与轴平行;位置为中心点坐标。
4. 除图中特殊注明外,孔洞翻边均高出板顶20
5. 由于土建专业修改情况较多,本次开版以出线示意,仅供

版次	日期	状态	修改-说明
C	2025.04	CFC	根据上游最新提资升版
B	2024.06	CFC	根据上游最新提资升版
A	2023.09	CFC	初版

浙江金七门核电厂1、2号机组

DOC.NO J D 1 N H H 1 1 0 0 4 B 2 5 C 4 2 S D

本文件产权属中国核电工程有限公司(CNPE)所有,未经书面许可,不得以任何方式复制、传播、发表和外借。
This document is the property of China Nuclear Power Engineering CO.,LTD (CNPE), no part of this document may beproduced by any means, nor transmitted without the written permission of CNPE.

中国核电工程有限公司
China Nuclear Power Engineering Co., Ltd

CNPE

工程号	2016	子项号	NH
图号	20161NH-JGS03-004		

核岛厂房 1NH
工程名称 反应堆厂房高楼板顶视模板图

图幅	A0
专业	结构
比例	1:75
共1张 第1张	

会签

工程	签字及日期